


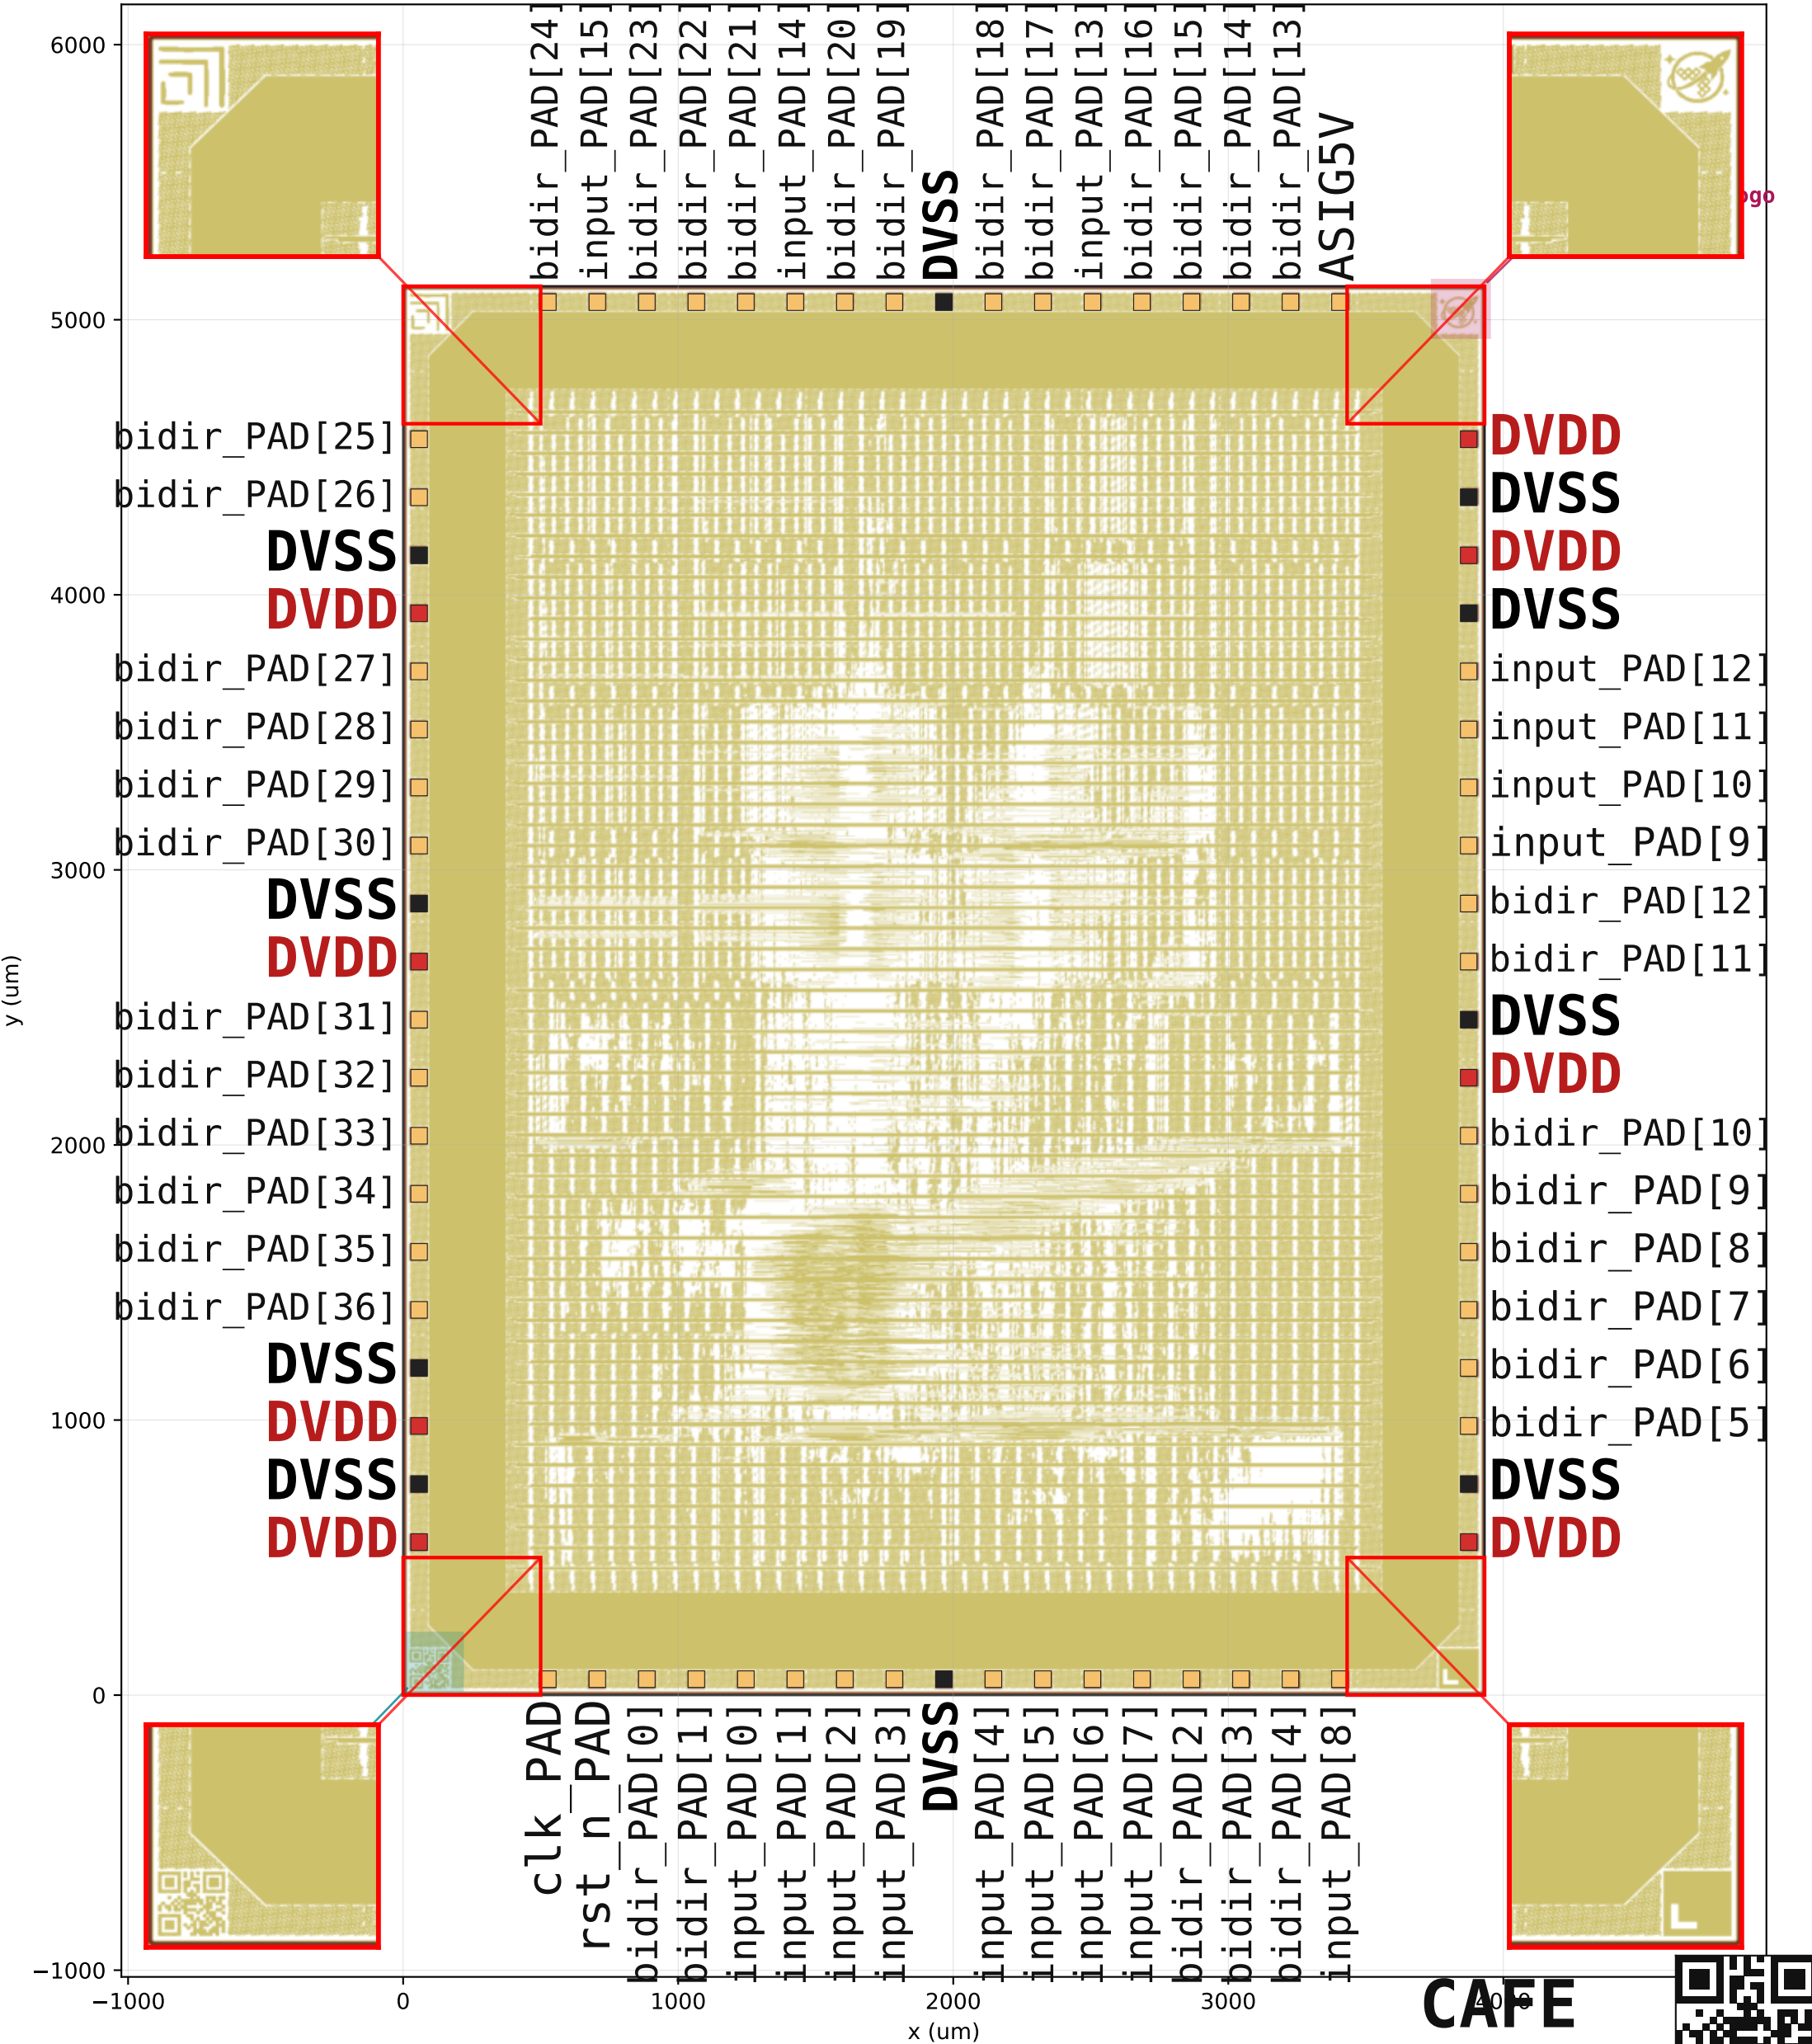

CAFE

slot 1x1